


КОМПАС-3D v23. Учебная версия © 2024. ООО "АСКОН-Системы проектирования". Россия. Все права защищены.
Инв. № подл. Подп. и дата. Инв. № докл. Подп. и дата. Инв. № докл. Подп. и дата.

Справ. №
Перв. примен.

31 000'00'00

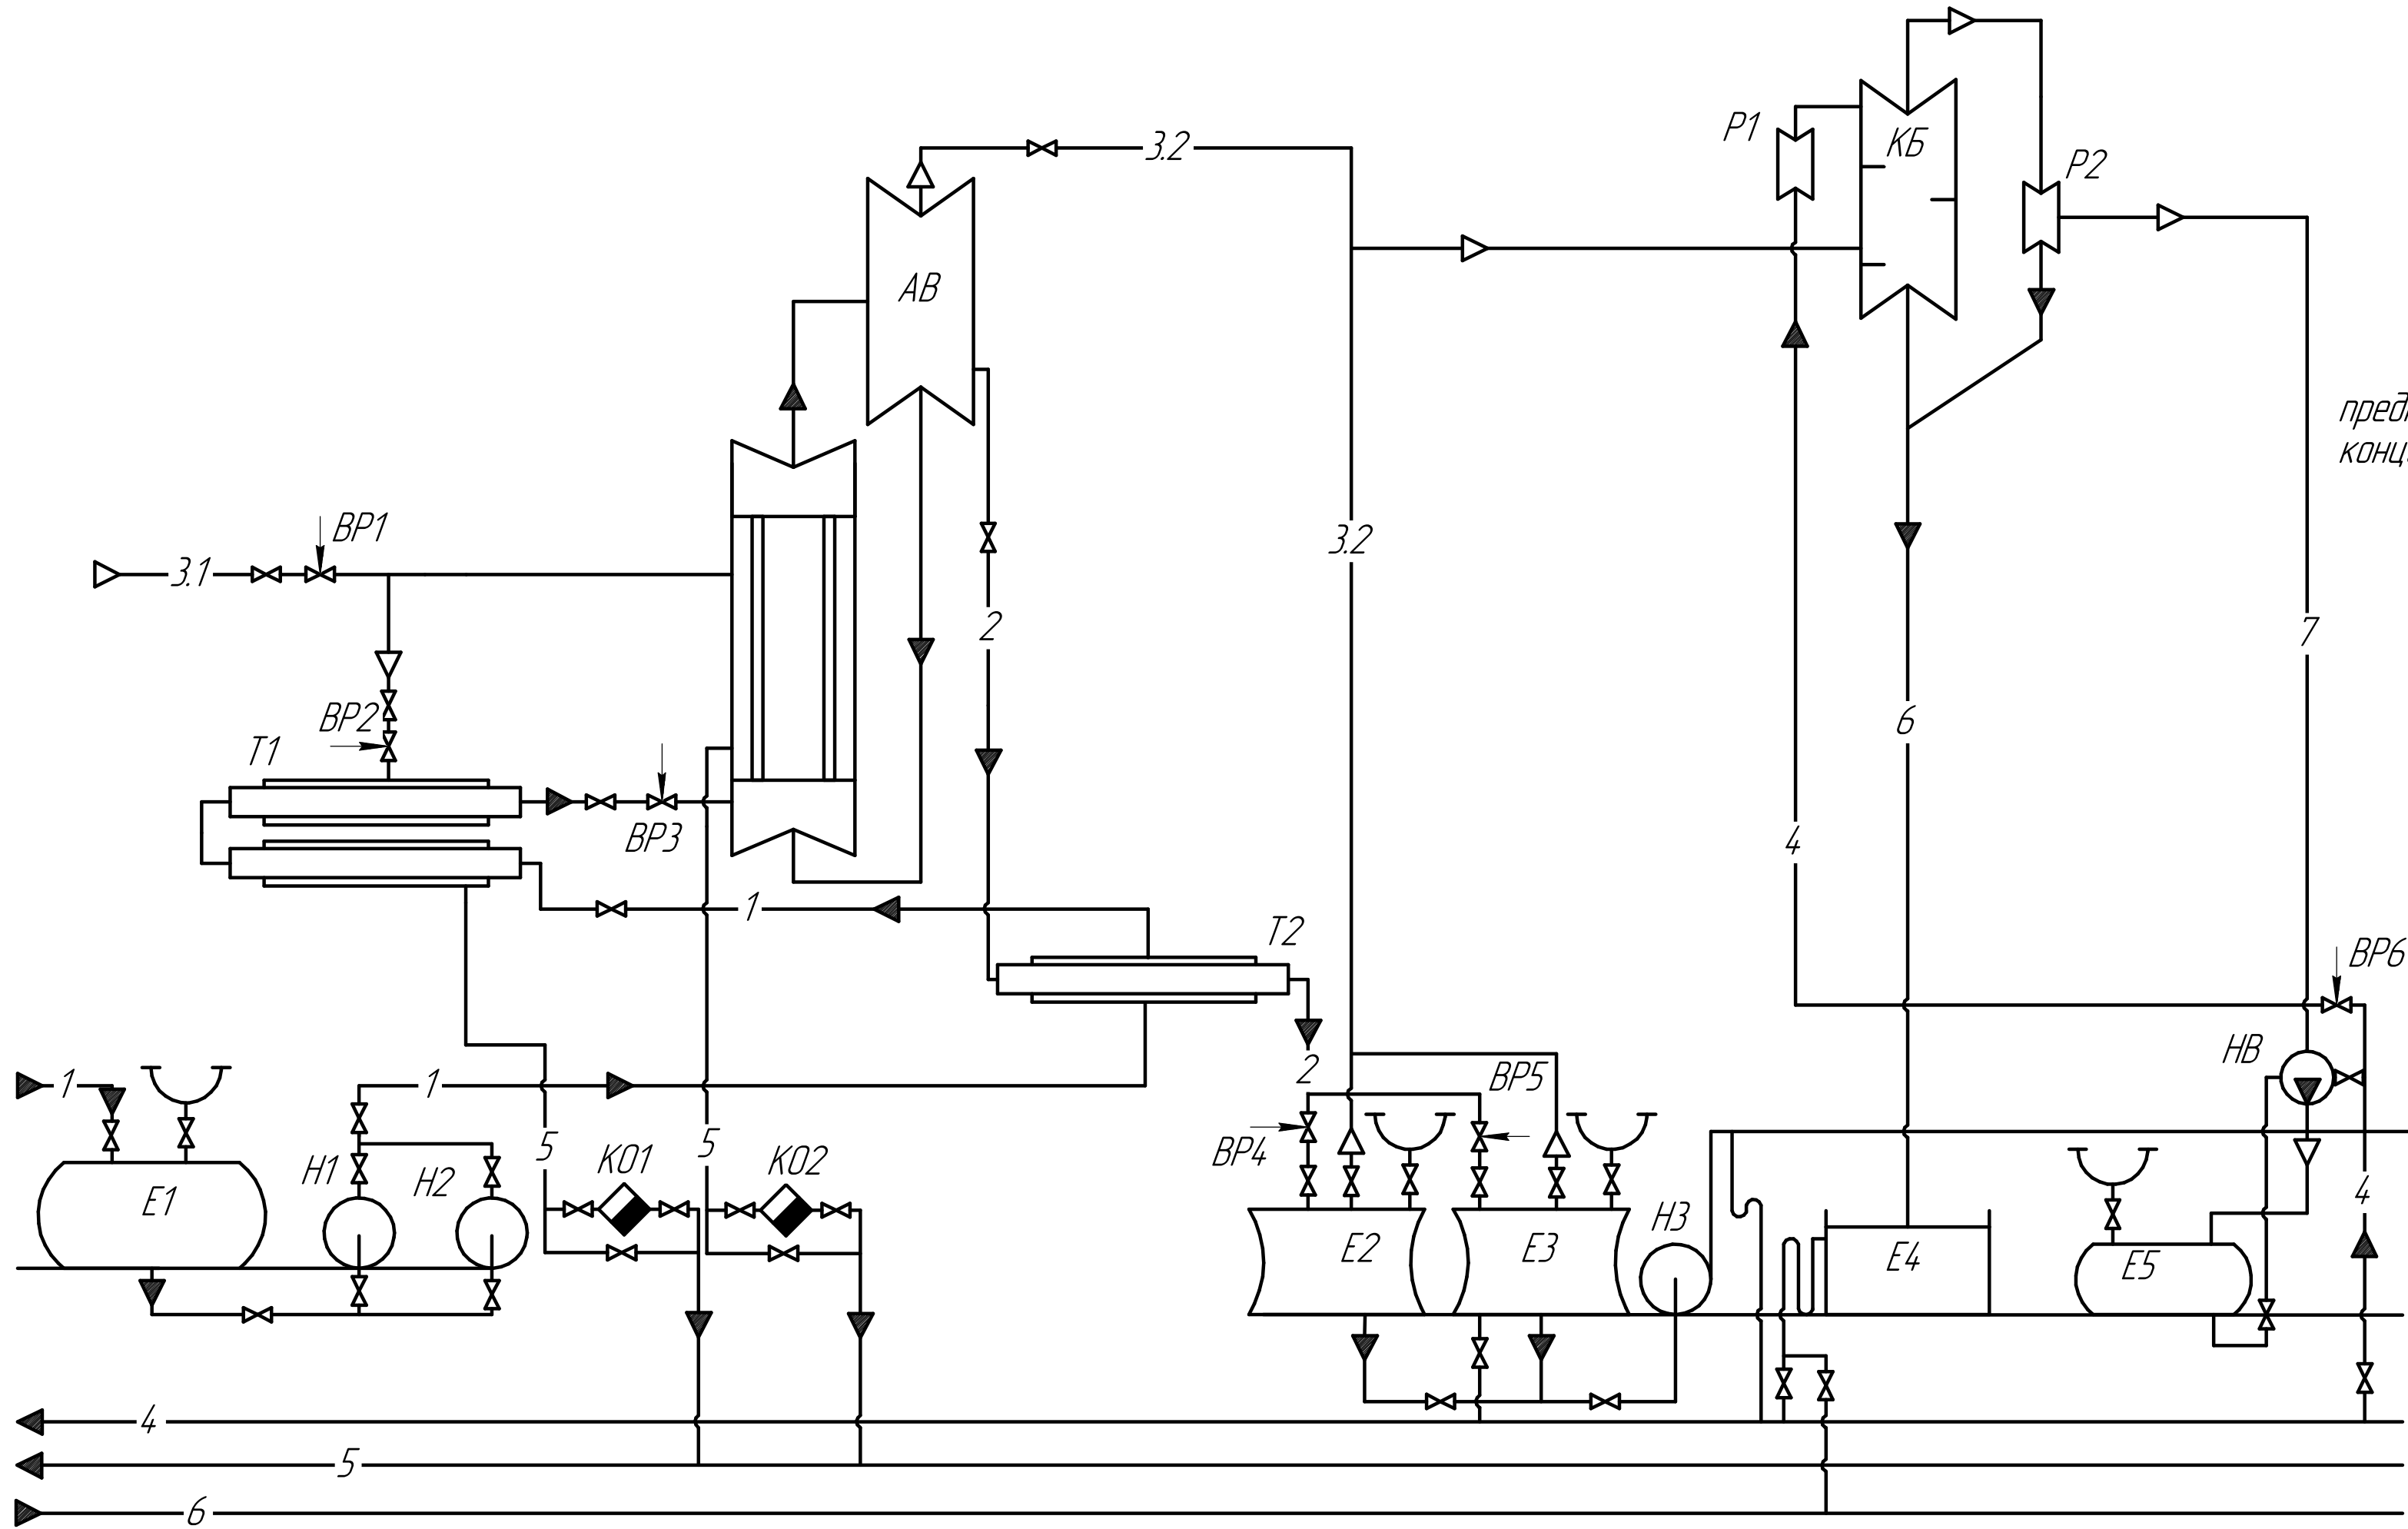

Обозначения трубопроводов	
Условное обозначение	Наименование среды в трубопроводе
1	Исходный раствор
2	Конечный раствор
3.1	Греющий пар
3.2	Вторичный пар
4	Вода
5	Конденсат
6	Вода обратная
7	Воздух

- 1 Однокорпусная вакуум-выпарная установка предназначена для выпаривания р-ра NH₄Cl с начальной концентрацией 3% до конечной концентрации 9%.
- 2 Давление греющего пара 0,1461 ат.
- 3 Температура греющего пара 110°C.
- 4 Вакуум в конденсаторе 0,615 ат.

Поз.	Наименование	Кол.	Примечание
AB	Аппарат выпарной	1	
T1-2	Теплообменник	2	
KB	Конденсатор барометрический	1	
P1-2	Расширитель	2	
E1-5	Емкость	5	
H1-3	Насос	3	
HВ	Насос воздушный	1	
BP1-6	Вентиль регулирующий	7	
KO1-2	Конденсатоотводчик	2	

00.00.000 ТС

Технологическая схема				Лит.	Масса	Масштаб
Изм.	Лист	№ докум.	Подп.	Дата		
Разраб.						
Проб.						
Т.контр.						
Н.контр.						
Утв.						
				Лист	Листов	1
				СПбГТИ(ТУ) гр. 124		
				Копировал Формат А2		