


Справ. №	Перв. примен.
----------	---------------

Подп. и дата	Инв. № дробл.	Взам. инв. №
--------------	---------------	--------------

Инв. № подл.	Подп. и дата
--------------	--------------

М400.4 7.00.08

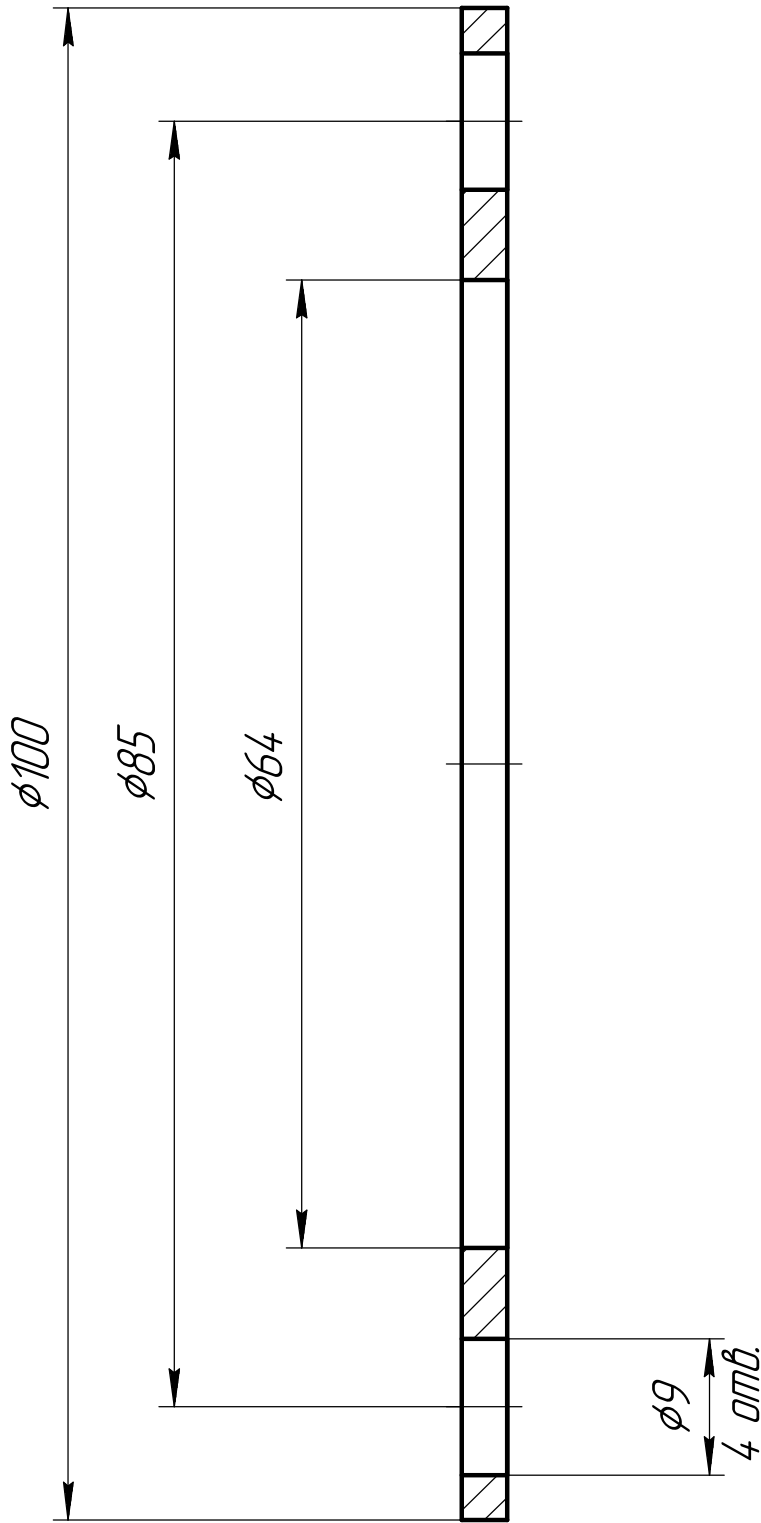

Изм.	Лист	№ докум.	Подп.	Дата
Разраб.	Акетов			
Пров.	Хайдаров			
Т.контр.				
Н.контр.				
Утв.				

М400.4 7.00.08			
Прокладка	Лист	Масса	Масштаб
			2:1
	Лист	Листов	1
	124 группа		