


КОМПАС-3D v23 Учебная версия © 2024 ООО "АСКОН-Системы проектирования", Россия Все права защищены.

|        |              |              |              |              |          |               |
|--------|--------------|--------------|--------------|--------------|----------|---------------|
| Изм. № | Подп. и дата | Взам. инв. № | Инв. № дубл. | Подп. и дата | Справ. № | Перв. примен. |
|        |              |              |              |              |          |               |

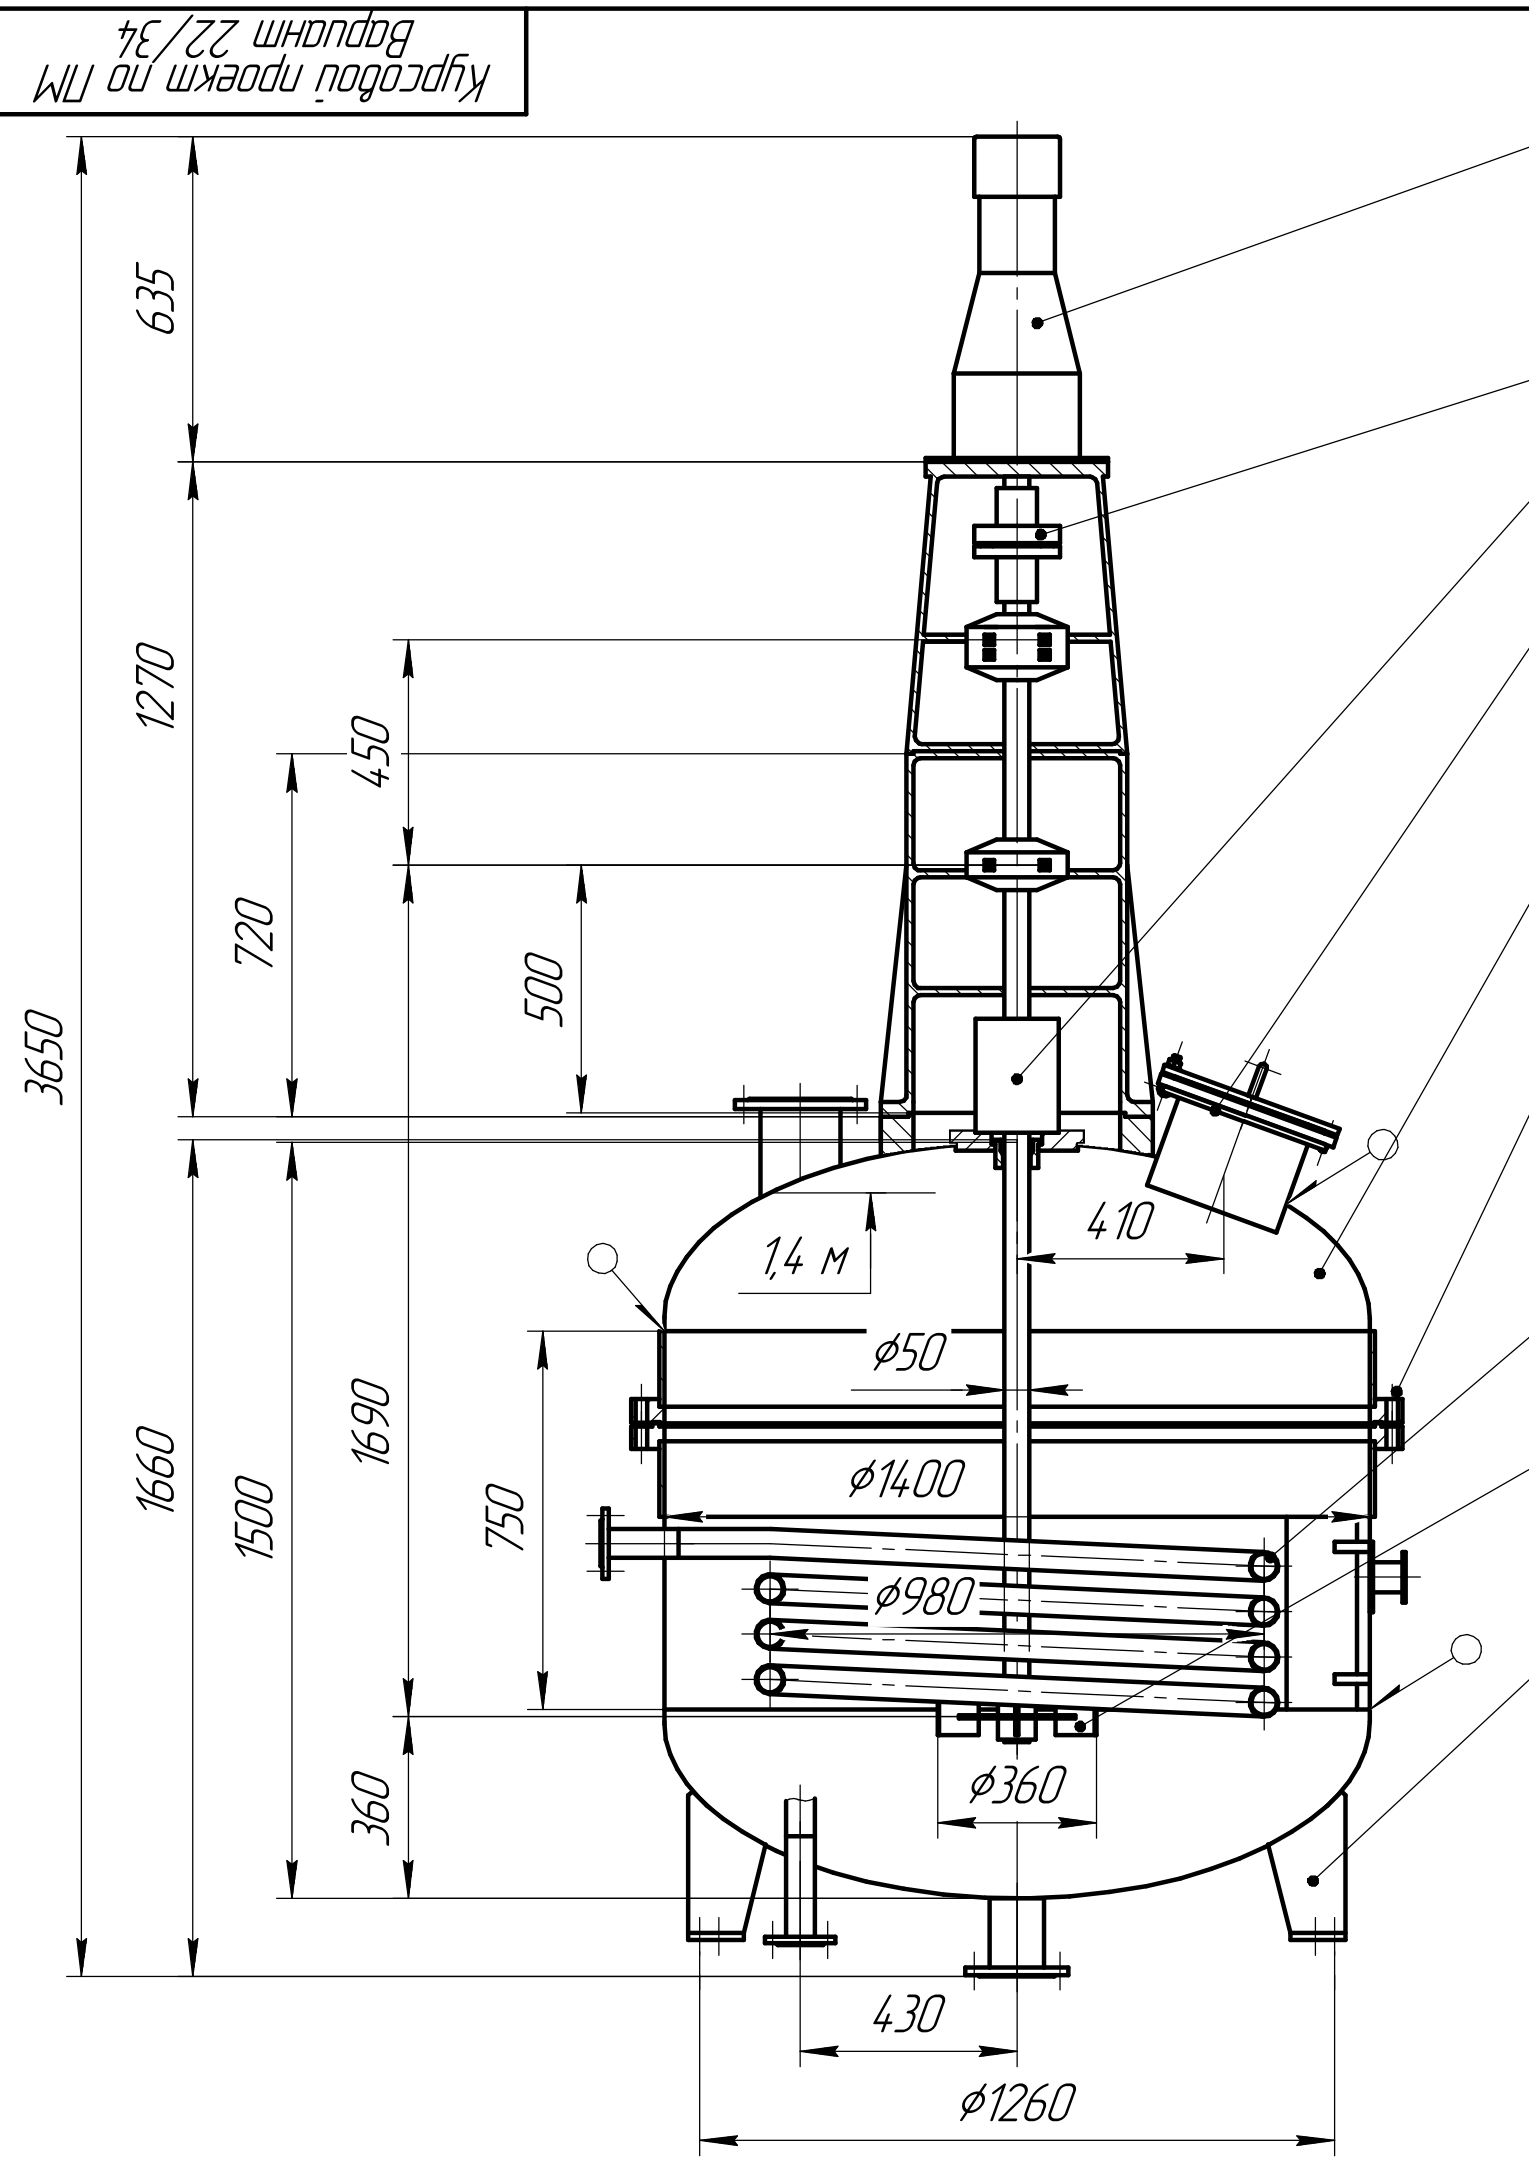

- Курсовой проект по ПМ  
Вариант 22/34
- Привод 13-1-50-3,0-250  
Стойка, чугуn СЧ 15 ГОСТ 1412-85  
Мотор-редуктор МП01М-10  
Муфта МУВП 0,5-65-1, сталь 40 ГОСТ 1050-88  
Уплотнение ТЗ-50-0,6 АТК 24.201.13-90  
Люк 2-250-0,6, ОСТ 26-2004-83, сталь 12Х18Н10Т ГОСТ 5632-72  
Прокладка 1-250-0,6, Паронит электролизерный ГОСТ 481-80  
Корпус ВЗЗ-2-2,0-1400 ГОСТ 9931-85 сталь 12Х18Н10Т ГОСТ 5632-72  
Цапфа 4-1-1-750, ГОСТ 13716-73, сталь СтЗсп ГОСТ 380-2005  
Змеевик (труба 57x3 ГОСТ 9941-81), сталь 12Х18Н10Т ГОСТ 5632-72  
Мешалка ОЗ-1-360, АТК 24.201.17-90, Сталь 12Х18Н10Т ГОСТ 5632-72  
Опорная-стойка 1-1-10 АТК 24.200.03-90, сталь СтЗсп ГОСТ 380-2005

|          |          |          |       |      |                                        |  |  |          |        |         |
|----------|----------|----------|-------|------|----------------------------------------|--|--|----------|--------|---------|
|          |          |          |       |      | Курсовой проект по ПМ<br>Вариант 22/34 |  |  |          |        |         |
|          |          |          |       |      | Аппарат с мешалкой                     |  |  | Лит.     | Масса  | Масштаб |
| Изм.     | Лист     | № докум. | Подп. | Дата |                                        |  |  |          |        | 1:15    |
| Разраб.  | Круглова |          |       |      |                                        |  |  |          |        |         |
| Пров.    |          |          |       |      |                                        |  |  |          |        |         |
| Т.контр. |          |          |       |      |                                        |  |  |          |        |         |
|          |          |          |       |      | Кафедра механики                       |  |  | Лист     | Листов | 1       |
| Н.контр. |          |          |       |      |                                        |  |  |          |        |         |
| Утв.     |          |          |       |      |                                        |  |  |          |        |         |
|          |          |          |       |      |                                        |  |  | гр. 1031 |        |         |