


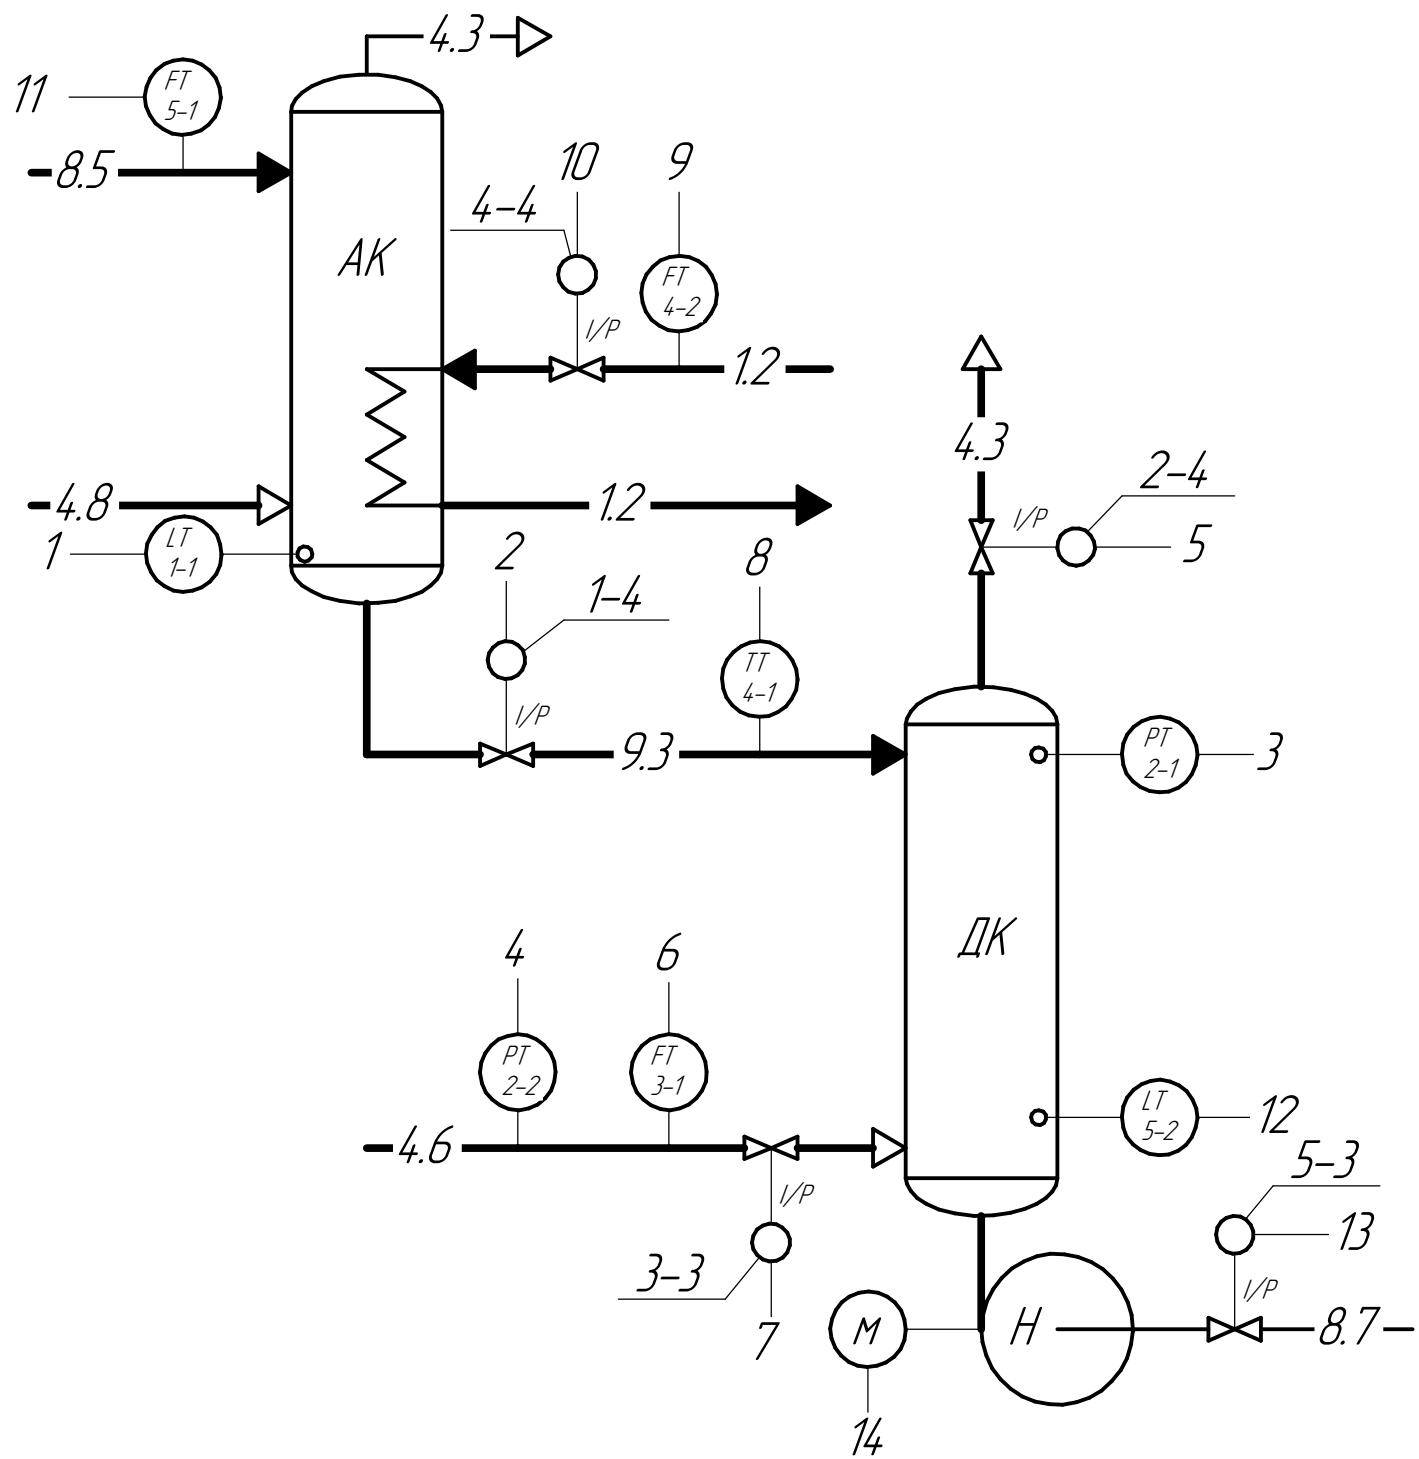

Условное обозначение трубопроводов

Обозначение	Содержимое трубопровода
1.2	Вода техническая
4.3	Ацетилен
4.6	Синтез-газ
4.8	Газ после пиролиза
8.5	ДМФ
8.7	Абсорбированный диацетилен
9.3	Насыщенный абсорбент

Перечень технологического оборудования

Обозначение	Наименование
AK	Абсорбционная колонна
ДК	Десорбционная колонна
H	Насос

Примечание
1. Условные графические и символьные обозначения выполнены согласно ГОСТ 21.208-2013 и ГОСТ 21.408-2013
2. Обозначения содержимых трубопроводов по ГОСТ 14.202-69.
3. Сигнализация:
HL1 – уровень L1 с датчика 1-1 больше $L1_{MAX}$
HL2 – давление P2 с датчика 2-1 больше $P2_{MAX}$
HL3 – уровень L6 с датчика 5-2 меньше $L6_{MIN}$
HL4 – уровень L6 с датчика 5-2 больше $L6_{MAX}$
HL5 – состояние клапана 5-3
4. I/P – преобразование электрического сигнала в пневматический
5. Дополнительные буквенные обозначения
а – давление с датчика 2-1
б – давление с датчика 2-2
в – расход с датчика 3-1
г – температура с датчика 4-1
д – расход с датчика 4-2
е – расход с датчика 5-1
ж – уровень с датчика 5-2
з – состояние клапана 5-3
МП – местные приборы; ПЛК – программируемый логический контроллер
ЩУ – щит управления; СО – станция оператора

		1	2	3	4	5	6	7	8	9	10	11	12	13	14			
Приборы местные																		
	Щит управления	 	 		 а, б, в, г д, е, ж, з													
ПЛК	УСО	AI1	AO1	AI2	AI3	AO2	AI4	AO3	AI5	AI6	AO4	AI7	AI8	DI1	DO1			
	С	•	•	•	•	•	•	•	•	•	•	•	•	•	•			
	У						•	•										
	С																	
СО	I,R	•		•	•		•		•		•	•	•	•	•			
	A	•		•									•	•				
	Н,К		•	•	•		•		•	•	•				•			

Изм.	Лист	№ докум.	Подп.	Дата	Лит.	Масса	Масштаб
Разраб.							
Проб.							
Т.контр.					Лист	Листов	1
Н.контр.							
Утв.							